SERVIU

SERVICIO DE VIVIENDA Y URBANIZACION
REGION METROPOLITANA
SUB–DIRECCION PAVIMENTACION Y OBRAS VIALES

SECCIÓN REVISIÓN E INSPECCIÓN DE PROYECTOS Y OBRAS DE PAVIMENTACIÓN Y AGUAS LLUVIAS PARTICULARES

PROYECTO DE PAVIMENTACION

URBANIZACION
LOTEO LO RECABARREN

TIPO DE VIA: SANTA MARIA (COLECTORA)
TIPO DE VIA: CAMINO AGUA DE PALO (COLECTORA)
TIPO DE VIA: CALLE GARCIA TELLO (AL)

PLANTA DE AGUAS LLUVIAS (CONTINUACION)/ DETALLES

COMUNA	FECHA	ESCALAS
VITACURA	SEPTIEMBRE 2025	INDICADAS

PROYECTO		TOPOGRAFIA
URBANO PROYECTOS	IVAN MUÑOZ S.–URBANO PROYECTOS Ing. Civil U. Ae Ch. Alfredo Barros Errazuriz 1953 Oficina 903 Fono 229125500	
LABORATORIO MECANICA DE SUELO	MANDANTE	OTRO
	INMOBILIARIA LO RECABARREN LTDA.	

APROBACION SERVIU METROPOLITANO

EL PRESENTE PLANO HA SIDO APROBADO POR OFICIO SERVIU
N° AE FECHA


REVISOR INGENIERO JEFE DE SECCION

CARPETA N°74073 PLANO N° 2 DE 5


N°	MOAIFICACION	FIRMA	FECHA
1	PARA APROBACION SERVIU	I.M.S.	SEP 2025
0	PARA APROBACION SERVIU	I.M.S.	12.11.24

ARCHIVO CAD : 31802_all ext_Urbanizacion loteo Lo Recabarren_ Rev 1.dwg

PLANTA DE AGUAS LLUVIAS
ESCALA 1 : 500

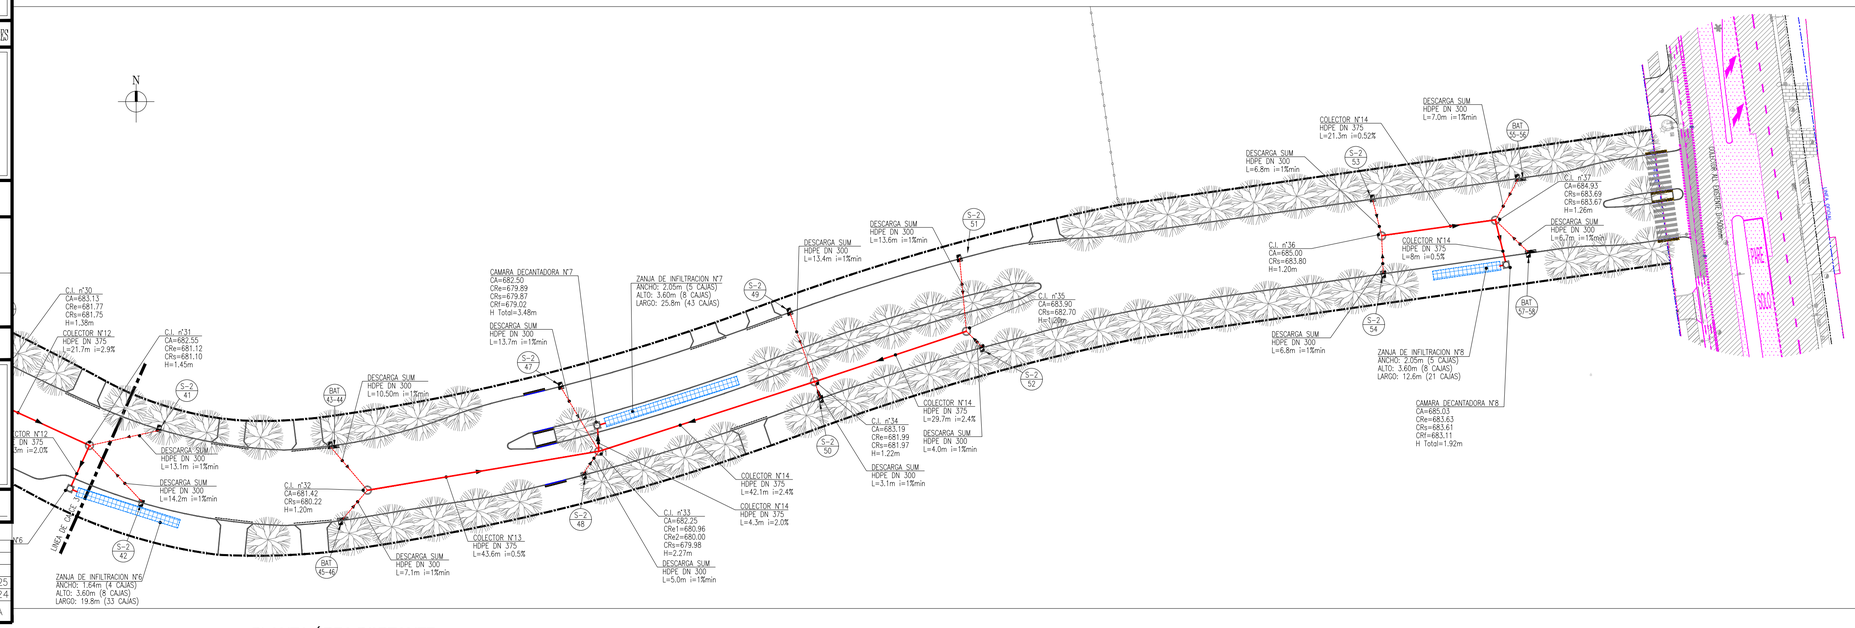

PLANTA ÁREA PORTANTE
ESCALA 1 : 2500

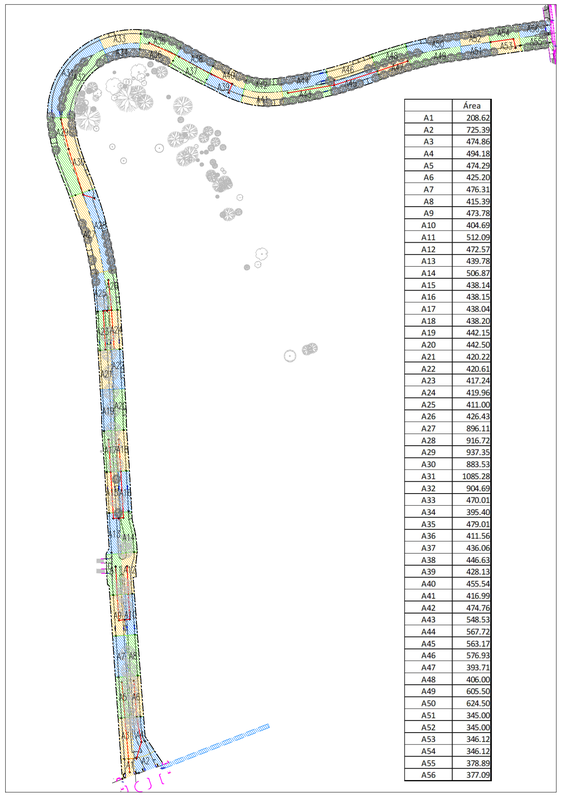

	Área
A1	208.62
A2	725.39
A3	474.86
A4	494.18
A5	474.29
A6	425.20
A7	476.31
A8	415.39
A9	473.78
A10	404.69
A11	512.09
A12	472.57
A13	439.78
A14	506.87
A15	438.14
A16	438.15
A17	438.04
A18	438.20
A19	442.15
A20	442.50
A21	420.22
A22	420.61
A23	417.24
A24	419.96
A25	411.00
A26	426.43
A27	896.11
A28	916.72
A29	937.35
A30	883.53
A31	1085.28
A32	904.69
A33	470.01
A34	395.40
A35	479.01
A36	411.56
A37	436.06
A38	446.63
A39	428.13
A40	455.54
A41	416.99
A42	474.76
A43	548.53
A44	567.72
A45	563.17
A46	576.93
A47	393.71
A48	406.00
A49	605.50
A50	624.50
A51	345.00
A52	345.00
A53	346.12
A54	346.12
A55	378.89
A56	377.09

CUADRO DE CAMARAS

CAMARA Nº	TIPO Y RADIER	DIAMETRO CAMARA (m)	DIAMETRO CANALETA (mm)	ALTURAS (m) TOTAL (H)	ALTURAS (m) CUERPO (h)	ALTURAS (m) CHIMENEA (h1)	TAPA TIPO CALZADA	Nº DE ESCALINES	SATELITE REFUERZO	CAIDA EXTERIOR
1	esp - 1	1,30	375	1,20	-	-	1	1	1	-
2	b 1	1,30	375	1,71	0,99	-	1	3	1	-
3	esp 1	1,30	375	1,29	-	-	1	2	1	-
4	esp 1	1,30	375	1,20	-	-	1	1	1	-
5	b 1	1,30	375	1,33	0,61	-	1	2	1	-
6	esp 1	1,30	375	1,26	-	-	1	1	1	-
7	esp 1	1,30	375	1,20	-	-	1	1	1	-
8	b 1	1,30	375	1,44	0,72	-	1	2	1	-
9	esp - 1	1,30	375	1,23	-	-	1	1	1	-
10	esp 1	1,30	375	1,20	-	-	1	1	1	-
11	b 1	1,30	375	1,55	0,83	-	1	2	1	-
12	esp 1	1,30	375	1,27	-	-	1	1	1	-
13	esp 1	1,30	375	1,20	-	-	1	1	1	-
14	b 1	1,30	375	1,44	0,72	-	1	2	1	-
15	esp 1	1,30	375	1,30	-	-	1	2	1	-
16	esp 1	1,30	375	1,20	-	-	1	1	1	-
17	b - 1	1,30	375	1,43	0,71	-	1	2	1	-
18	esp 1	1,30	375	1,30	-	-	1	2	1	-
19	esp 1	1,30	375	1,20	-	-	1	1	1	-
20	esp 1	1,30	375	1,20	-	-	1	1	1	-
21	b 1	1,30	375	1,68	0,96	-	1	3	1	-
22	esp 1	1,30	375	1,20	-	-	1	1	1	-
23	b 1	1,30	375	1,79	1,07	-	1	3	1	-
24	esp - 1	1,30	375	1,20	-	-	1	1	1	-
25	b 1	1,30	375	1,33	0,61	-	1	2	1	-
26	esp 1	1,30	375	1,23	-	-	1	1	1	-
27	esp 1	1,30	375	1,20	-	-	1	1	1	-
28	esp 1	1,30	375	1,20	-	-	1	1	1	-
29	esp 1	1,30	375	1,31	-	-	1	2	1	-
30	b 1	1,30	375	1,38	0,66	-	1	2	1	-
31	b 1	1,30	375	1,45	0,73	-	1	2	1	-
32	esp - 1	1,30	375	1,20	-	-	1	1	1	-
33	a 1	1,30	375	2,27	0,95	0,25	1	5	1	-
34	esp 1	1,30	375	1,22	-	-	1	1	1	-
35	esp 1	1,30	375	1,20	-	-	1	1	1	-
36	esp 1	1,30	375	1,20	-	-	1	1	1	-
37	esp 1	1,30	375	1,26	-	-	1	1	1	-

CUADRO DE CAÑERIAS

MATERIAL (HDPE) - DIAMETRO (mm) - LONGITUD (m)	HDPE	
DESIGNACION	300	375
	(m)	(m)
COLECTORES	-	899
CAÑERIAS DESCARGAS SUMIDEROS	385	-
TOTAL	385	899

RESUMEN CAMARAS DE INSPECCION

Cámaras tipo "a" DCuerpo 1.30	Hm =	2,27 m.	Nº	1
Cámaras tipo "b" DCuerpo 1.30	Hm =	1,50 m.	Nº	11
Cámaras especiales	Hm =	1,23 m.	Nº	25
Camaras decantadoras dobles			Nº	0
TOTAL			Nº	37
Tapas tipo calzada			Nº	37
Escalines			Nº	59
Satélite de refuerzo			Nº	37

CUADRO DE SUMIDEROS

SUMIDERO Nº	TIPO SUMIDERO	CONEXIÓN A	LONGITUD UNION (m)
1	S-2	C.I. Nº1	9,90
2	S-2	C.I Existente	2,00
3-4	BAT	C.I. Nº2	3,70
5-6	BAT	C.I. Nº5	3,00
7	S-2	C.I. Nº3	3,00
8	S-2	C.I. Nº6	3,20
9	S-2	C.I. Nº4	5,40
10	S-2	C.I. Nº7	5,80
11	S-2	C.I. Nº8	14,60
12	S-2	C.I. Nº11	15,00
13	S-2	C.I. Nº9	3,50
14	S-2	C.I. Nº12	3,20
15	S-2	C.I. Nº10	11,90
16	S-2	C.I. Nº13	14,50
17	S-2	C.I. Nº14	6,20
18	S-2	C.I. Nº17	7,30
19	S-2	C.I. Nº15	3,30
20	S-2	C.I. Nº18	4,70
21	S-2	C.I. Nº16	9,00
22	S-2	C.I. Nº19	9,70
23	S-2	C.I. Nº20	4,80
24	S-2	C.I. Nº22	4,80
25	S-2	C.I. Nº21	4,70
26	S-2	C.I. Nº23	5,00
27-28	BAT	C.I. Nº24	12,60
29-30	BAT	C.I. Nº24	9,10
31	S-3	C.I. Nº25	7,20
32	S-3	C.I. Nº25	6,90
33	S-2	C.I. Nº27	7,40
34	S-2	C.I. Nº27	7,50
35	S-2	C.I. Nº28	11,20
36	S-2	C.I. Nº28	10,30
37	S-2	C.I. Nº29	8,30
38	S-3	C.I. Nº29	6,90
39	S-2	C.I. Nº30	7,50
40	S-3	C.I. Nº30	6,40
41	S-2	C.I. Nº31	13,10
42	S-2	C.I. Nº31	14,20
43-44	BAT	C.I. Nº32	10,50
45-46	BAT	C.I. Nº32	7,10
47	S-2	C.I. Nº33	13,70
48	S-2	C.I. Nº33	5,00
49	S-2	C.I. Nº34	13,40
50	S-2	C.I. Nº34	3,10
51	S-2	C.I. Nº35	13,60
52	S-2	C.I. Nº35	4,00
53	S-2	C.I. Nº36	6,80
54	S-2	C.I. Nº36	6,80
55-56	BAT	C.I. Nº37	7,00
57-58	BAT	C.I. Nº37	6,70
		TOTAL	384,50

REVISION N°		EJECUTÓ	AIBUJÓ	REVISÓ	APROBÓ	FECHA
0	PARA APROBACION SERVIU	V.A.F.	V.A.F.	L.E.C.	I.M.S.	12.11.24

ARCHIVO CAD : 31802_all ext_Urbanizacion loteo Lo Recabarren_Rev 1.dwg