SERVIU

SERVICIO DE VIVIENDA Y URBANIZACION
REGION METROPOLITANA
SUB–DIRECCION PAVIMENTACION Y OBRAS VIALES

SECCIÓN REVISIÓN E INSPECCIÓN DE PROYECTOS Y OBRAS DE PAVIMENTACIÓN Y AGUAS LLUVIAS PARTICULARES

PROYECTO DE PAVIMENTACION

URBANIZACION
LOTEO LO RECABARREN

TIPO DE VIA: SANTA MARIA (COLECTORA)
TIPO DE VIA: CAMINO AGUA DE PALO (COLECTORA)
TIPO DE VIA: CALLE CAMINO LOCAL (LOCAL)

DETALLES AGUAS LLUVIAS (CONTINUACION)

COMUNA	FECHA	ESCALAS
VITACURA	SEPTIEMBRE 2025	INDICADAS

PROYECTO		TOPOGRAFIA
URBANO PROYECTOS	IVAN MUÑOZ S.–URBANO PROYECTOS Ing. Civil U. Ae Ch. Alfredo Barros Errazuriz 1953 Oficina 903 Fono 229125500	
LABORATORIO MECANICA DE SUELO	MANDANTE	OTRO
	INMOBILIARIA LO RECABARREN LTDA.	

APROBACION SERVIU METROPOLITANO

EL PRESENTE PLANO HA SIDO APROBADO POR OFICIO SERVIU
N° AE FECHA

REVISOR INGENIERO JEFE DE SECCION


CARPETA N°74073 PLANO N° 4 DE 5

N°	MODIFICACION	FIRMA	FECHA
1	PARA APROBACION SERVIU	I.M.S.	SEP 2025
0	PARA APROBACION SERVIU	I.M.S.	12.11.24

ARCHIVO CAD : 31802_all ext_Urbanizacion loteo Lo Recabarren_Rev 1.dwg


ZANJA DREN DE INFILTRACION N°4 MODULOS 7x8
PROYECTADO BAJO AREA VERDE

ESCALA 1 : 25

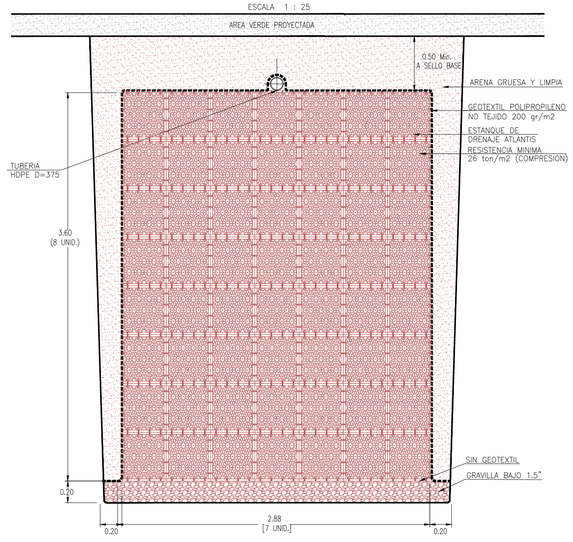


ZANJA DREN DE INFILTRACION N°3 MODULOS 6x8
PROYECTADO BAJO AREA VERDE

ESCALA 1 : 25

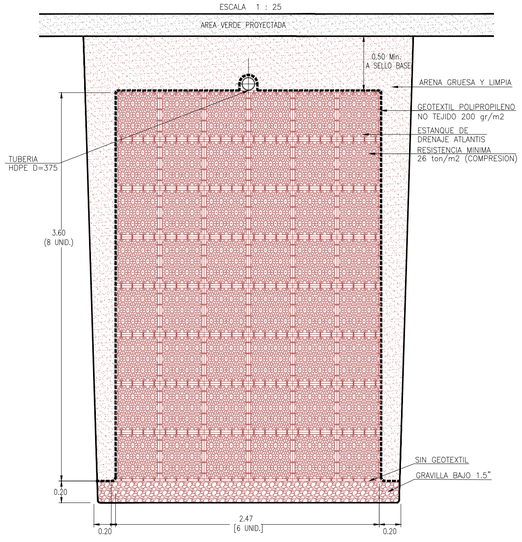


ZANJA DREN DE INFILTRACION N°1 MODULOS 13x9
PROYECTADO BAJO AREA VERDE

ESCALA 1 : 25

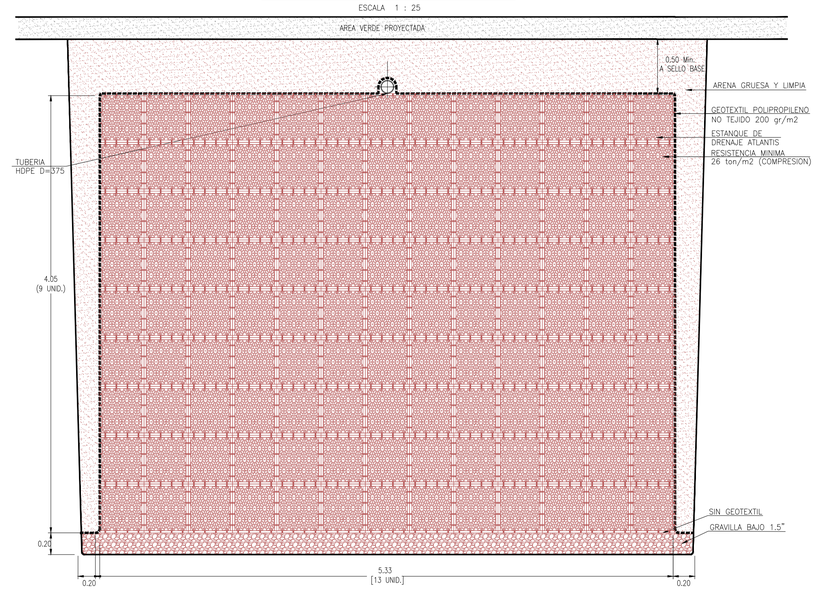

PERFIL LONGITUDINAL COLECTOR 14

ESCALA HORIZONTAL 1:500
ESCALA VERTICAL 1:50

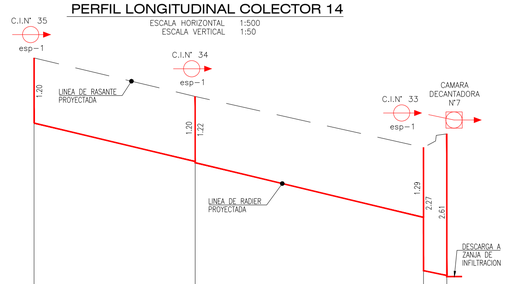


679.5									
DISTANCIAS PARCIALES, ACUMULADAS Y ENTRE CAMARAS	0.0	29.7		29.7	42.1		71.8	4.3	76.1
COTAS DE ANILLO	683.90			683.19			682.25	682.50	
COTAS DE RADIER	682.70			681.99 681.97			680.06 679.98	679.89 679.87	
DIAMETROS Y PENDIENTES		COLECTOR HDPE DN 375 i=2.4%			COLECTOR HDPE DN 375 i=2.4%			C. HDPE DN 375 i=2.0%	
VOLUMEN DE EXCAVACION 0–2		37.6			55.6			8.4	
2–4		"			"			2.4	
4–6		"			"			"	

(1) = COLECTOR HDPE DN 375 i=2.0%

PERFIL LONGITUDINAL COLECTOR 13


ESCALA HORIZONTAL 1:500
ESCALA VERTICAL 1:50

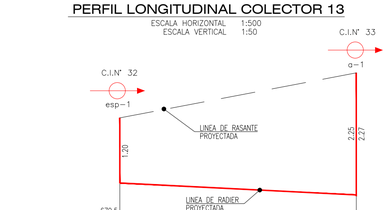

679.5				
DISTANCIAS PARCIALES, ACUMULADAS Y ENTRE CAMARAS	0.0	43.6		43.6
COTAS DE ANILLO	681.42			682.25
COTAS DE RADIER	680.22			680.00 679.98
DIAMETROS Y PENDIENTES		COLECTOR HDPE DN 375 i=2.4%		
VOLUMEN DE EXCAVACION 0–2		77.6		
2–4		"		
4–6		"		

PERFIL LONGITUDINAL COLECTOR 15

ESCALA HORIZONTAL 1:500
ESCALA VERTICAL 1:50

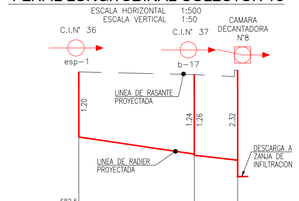


682.5					
DISTANCIAS PARCIALES, ACUMULADAS Y ENTRE CAMARAS	0.0	21.3	21.3	8.0	31.3
COTAS DE ANILLO	685.00		684.55		685.33
COTAS DE RADIER	683.80		683.69 683.67		683.51 683.47
DIAMETROS Y PENDIENTES		COLECTOR HDPE DN 375 i=0.52%		COLECTOR HDPE DN 375 i=0.5%	
VOLUMEN DE EXCAVACION 0–2		27.4		14.7	
2–4		"		"	
4–6		"		"	

(1) = COLECTOR HDPE DN 375 i=2.0%


ZANJA DREN DE INFILTRACION N°5–N°6 MODULOS 4x8
PROYECTADO BAJO AREA VERDE

ESCALA 1 : 25

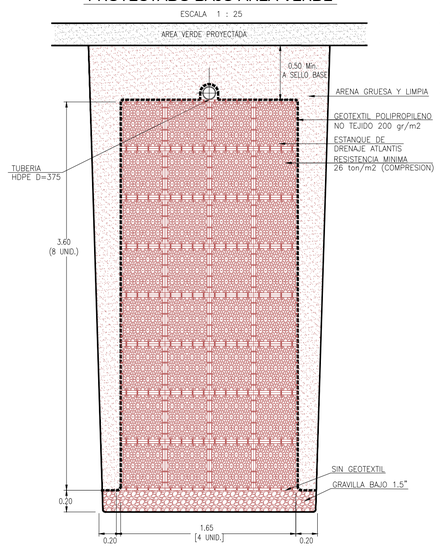


ZANJA DREN DE INFILTRACION N°2 - N°7 MODULOS 5x8
PROYECTADO BAJO AREA VERDE

ESCALA 1 : 25

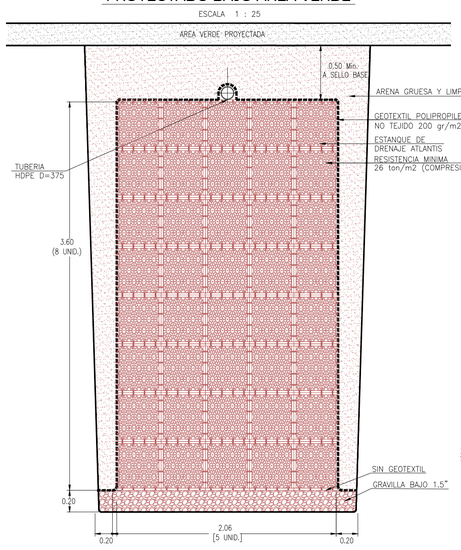

DETALLE CELDA DRENANTE


ESCALA 1 : 50

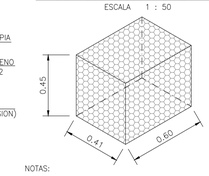

NOTAS:
- CADA MODULO ES FABRICADO DE PROLIPROPILENO
- LA UNION DE CADA CUBO ES SOLO DE TOPE
- LAS DIMENSIONES PUEDEN VARIAR DEPENDIENDO DEL FABRICANTE


TAPA CIRCULAR TIPO CALZADA

ESCALA 1 : 10

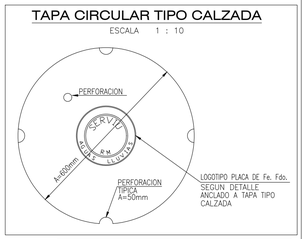


UNION CAÑERIA
AE HAPE A CAMARA

ESCALA 1:25

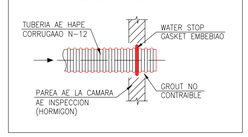

SISTEMA DE DRENAJE HIDROCELDA
TUBERIA EN ZANJA DE ACUMULACION

P L A N T A

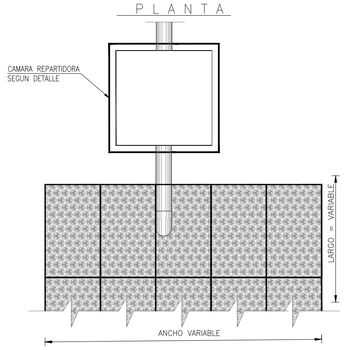

REVISION N°		EJECUTÓ	AIBUJÓ	REVISÓ	APROBÓ	FECHA
0	PARA APROBACION SERVIU	V.A.F.	V.A.F.	L.E.C.	I.M.S.	12.11.24

ARCHIVO CAD : 31802_all ext_Urbanizacion loteo Lo Recabarren_Rev 1.dwg