SERVIU

SERVICIO DE VIVIENDA Y URBANIZACION
REGION METROPOLITANA
SUB-DIRECCION PAVIMENTACION Y OBRAS VIALES

SECCIÓN REVISIÓN E INSPECCIÓN DE PROYECTOS Y OBRAS DE PAVIMENTACIÓN Y AGUAS LLUVIAS PARTICULARES

PROYECTO DE PAVIMENTACION

URBANIZACION
LOTEO LO RECABARREN

TIPO DE VIA: SANTA MARIA (COLECTORA)
TIPO DE VIA: CAMINO AGUA DE PALO (COLECTORA)
TIPO DE VIA: CALLE CASA TEJA (LOCAL)

DETALLES DE PAVIMENTACION

COMUNA	FECHA	ESCALAS
VITACURA	SEPTIEMBRE 2025	INDICADAS

PROYECTO		TOPOGRAFIA
URBANO PROYECTOS	IVAN MUÑOZ S.-URBANO PROYECTOS Ing. Civil U. de Ch. Alfredo Barros Errazuriz 1953 Oficina 303 Fono 229125500	
LABORATORIO MECANICA DE SUELO	MANDANTE	OTRO
	INMOBILIARIA LO RECABARREN LTDA.	

APROBACION SERVIU METROPOLITANO

EL PRESENTE PLANO HA SIDO APROBADO POR OFICIO SERVIU
N° DE FECHA

REVISOR | INGENIERO JEFE DE SECCION

CARPETA N°74073 PLANO N° 10 DE 10


1	PARA APROBACION SERVIU	I.M.S.	SEP 2025
0	PARA APROBACION SERVIU	I.M.S.	12.11.24
N°	MOAIFICACION	FIRMA	FECHA

ARCHIVO CAD : 31802_pav ext_Urbanizacion loteo Lo Recabarren_Rev 1.dwg

N O T A S :


- EL CBR DE LAS SUBRASANTE CONSIDERADO PARA EL DISEÑO DE LOS PAVIMENTOS ES IGUAL A 12%. AL MOMENTO DE EJECUTAR LA OBRA SE DEBERÁ VERIFICAR EL CBR A NIVEL DE SUBRASANTE, EN CASO DE SER DIFERENTE AL CBR DE DISEÑO, DEBERÁ REDISEÑAR LA ESTRUCTURA DE PAVIMENTO CONSIDERANDO CBR REAL Y CARTILLA DE DISEÑO DE PAVIMENTOS DEL SERVIU METROPOLITANO. ESTA SITUACIÓN SERÁ VERIFICADA POR EL ITO EN TERRENO.
- LA SUBRASANTE EN NINGÚN CASO PODRÁ ESTAR CONSTITUIDA POR SUELOS ORGÁNICOS Y/O ARCILLAS EXPANSIVAS.
- EL SUELO A NIVEL DE LA SUBRASANTE DEBERÁ ESCARIFICARSE EN UN ESPESOR MÍNIMO DE 0.20m., COMPACTÁNDOSE HASTA OBTENER UNA DENSIDAD MÍNIMA DEL 95% DEL ENSAYO DE PROCTOR MODIFICADO
- EL CBR DE LAS BASES ESTABILIZADA DEBERÁ SER MAYOR O IGUAL AL 60%
- EN CASO DE NO CUMPLIRSE CON ALGUNAS DE LAS CONDICIONES ANTERIORES SE DEBERÁ REEMPLAZAR EL SUELO NATURAL POR UNA SUBBASE GRANULAR DEL ESPESOR INDICADO EN LAS E.E.T.T. DEL PROYECTO Y/O PERFILES TIPO DEL PROYECTO
- LA INTERSECCIÓN ENTRE EL ACCESO Y LA VEREDA DEBERÁ ENCONTRASE AL MISMO NIVEL Y SU PAVIMENTO DEBERÁ ESTAR CONSTITUIDO POR UNA SUPERFICIE ANTIDESLIZANTE, EL CUAL SE PROLONGARÁ EN 1,00m., HACIA AMBOS LADOS DE LA INTERSECCIÓN.
- EL ACCESO SE DEBE CONSTRUIR DE ACUERDO A ESPECIFICACIONES TÉCNICAS DEL SERVIU
- LAS VEREDAS, TANTO EXISTENTES COMO PROYECTADAS, DEBERÁN ESTAR LIBRES DE OBSTÁCULOS , SITUACIÓN QUE SERÁ VERIFICADA POR TERRENO POR EL ITO
- LOS CORTES REALIZADOS EN LAS VEREDAS DEBEN SER A TRAVÉS DE MÉTODOS MECÁNICOS COMO CORTADORA DE PAVIMENTO, EN NINGÚN CASO SE PODRÁ EJECUTAR CORTES CON PLETINA, RODONES TRANSVERSALES O ALGÚN OTRO MÉTODO QUE GENERE UNA DEPRESIÓN ENTRE PAÑOS DE VEREDA CONTINUOS, ESTE ULTIMO SERÁ MOTIVO DE DEMOLICIÓN DE PAÑOS QUE SE ENCUENTREN EN DICHAS CONDICIONES
- SERÁ RESPONSABILIDAD EXCLUSIVA DEL CONTRATISTA O DE QUIEN SE ENCOMIENDE LA EJECUCIÓN DE LAS OBRAS CONTEMPLADAS EN EL PROYECTO, LOS COSTOS DERIVADOS DE MODIFICACIONES Y TRASLADO DE REDES DE SERVICIO PÚBLICOS, QUE NO HAYAN SIDO INTEGRADAS EN EL PROYECTO Y QUE EVENTUALMENTE INTERFIERAN CON LA REALIZACIÓN DE LAS OBRAS, ASÍ COMO TAMBIÉN LA OBTENCIÓN DE TODAS LAS AUTORIZACIONES, APROBACIONES, INSPECCIONES Y RECEPCIONES DE LAS OBRAS CORRESPONDIENTES, DE PARTE DE LAS RESPECTIVAS COMPAÑÍAS QUE SUMINISTREN DICHOS SERVICIOS.

DETALLE RESALTO - LOMO DE TORO PLANO CON PASO DE CEBRA

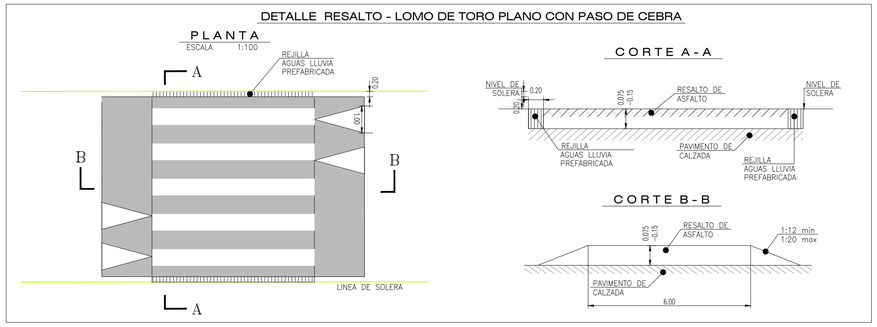


DETALLE TIPO BANDA DE ESTACIONAMIENTO LATERAL

ESCALA 1 : 50

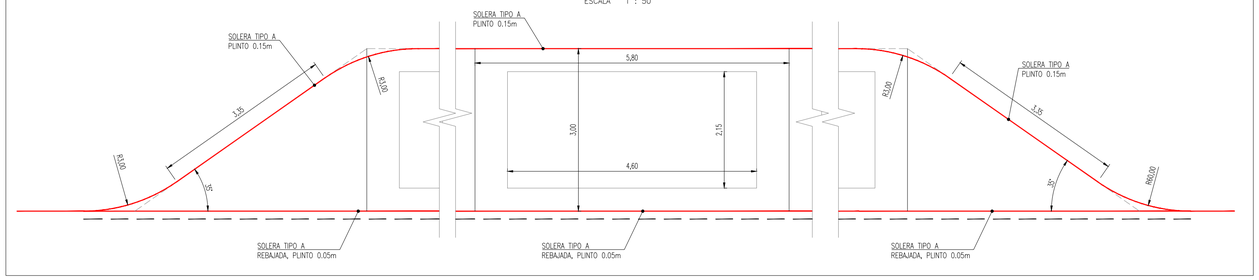


JUNTA TRANSVERSAL DE CONSTRUCCION CON BARRA DE TRASPASO

SIN ESCALA

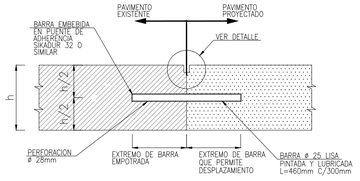

DETALLE
ESCALA 1 : 1

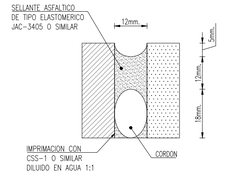


NOTA:


1. BARRAS DE TRASPASO DE CARGA ACERO SAE 1020.
2. EL EXTREMO DE LA BARRA QUE QUEDARA INSERTA EN EL PAVIMENTO NUEVO SE DEJA EMBEBIDO EN GRASA Y ENVUELTO EN POLIETILENO, EL CUAL SE RETIRARÁ AL MOMENTO DE VACIADO EL HORMIGON
3. EL MATERIAL DEL CORDON DEBE RESISTIR LA TEMPERATURA DE APLICACION DEL SELLO (CONSULTAR A DISTRIBUIDOR DEL PRODUCTO)

JUNTA LONGITUDINAL DE CONSTRUCCION CON BARRA DE TRASPASO

SIN ESCALA

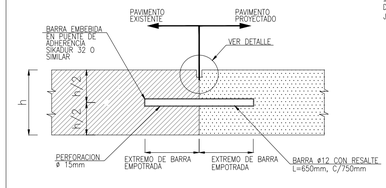

DETALLE
ESCALA 1 : 1

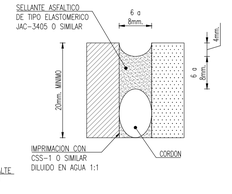


NOTA:

1. BARRAS DE TRASPASO DE CARGA ACERO A63-42H.
2. EL MATERIAL DEL CORDON DEBE RESISTIR LA TEMPERATURA DE APLICACION DEL SELLO (CONSULTAR A DISTRIBUIDOR DEL PRODUCTO)

JUNTA TRANSVERSAL DE CONTRACCION


SIN ESCALA

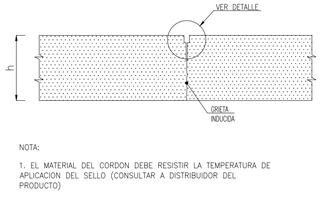

NOTA:

1. EL MATERIAL DEL CORDON DEBE RESISTIR LA TEMPERATURA DE APLICACION DEL SELLO (CONSULTAR A DISTRIBUIDOR DEL PRODUCTO)

DETALLE
ESCALA 1 : 1

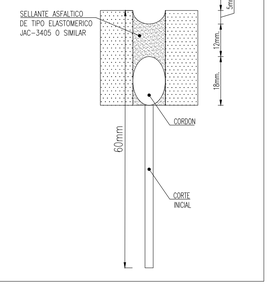

0	PARA APROBACION SERVIU	V.A.F.	V.A.F.	L.E.C.	I.M.S.	12.11.24
REVISION N°		EJECUTÓ	AIBUJÓ	REVISÓ	APROBÓ	FECHA

ARCHIVO CAD : 31802_pav ext_Urbanizacion loteo Lo Recabarren_Rev 1.dwg