SERVIU

SERVICIO DE VIVIENDA Y URBANIZACION
REGION METROPOLITANA
SUB–DIRECCION PAVIMENTACION Y OBRAS VIALES

SECCIÓN REVISIÓN E INSPECCIÓN DE PROYECTOS Y OBRAS DE PAVIMENTACIÓN Y AGUAS LLUVIAS PARTICULARES

PROYECTO DE PAVIMENTACION

URBANIZACION
LOTEO LO RECABARREN

TIPO DE VIA: SANTA MARIA (COLECTORA)
TIPO DE VIA: CAMINO AGUA DE PALO (COLECTORA)
TIPO DE VIA: CALLE CASA TEJA (LOCAL)

PLANTA DE DEMOLICION (CONTINUACION)

COMUNA	FECHA	ESCALAS
VITACURA	SEPTIEMBRE 2025	INDICADAS

PROYECTO		TOPOGRAFIA
URBANO PROYECTOS	IVAN MUÑOZ S.–URBANO PROYECTOS Ing. Civil U. de Ch. Alfredo Barros Errazuriz 1953 Oficina 903. Fono. 229125500	
LABORATORIO MECANICA DE SUELO	MANDANTE	OTRO
	INMOBILIARIA LO RECABARREN LTDA.	

APROBACION SERVIU METROPOLITANO

EL PRESENTE PLANO HA SIDO APROBADO POR OFICIO SERVIU
N° DE FECHA

REVISOR INGENIERO JEFE DE SECCION


CARPETA N°74073 PLANO N° 2 DE 10

N°	MODIFICACION	FIRMA	FECHA
1	PARA APROBACION SERVIU	I.M.S.	SEP 2025
0	PARA APROBACION SERVIU	I.M.S.	12.11.24

ARCHIVO CAD : 31802_pav ext_Urbanizacion loteo Lo Recabarren_Rev 1.dwg


PLANTA DE DEMOLICION

ESCALA 1 : 500

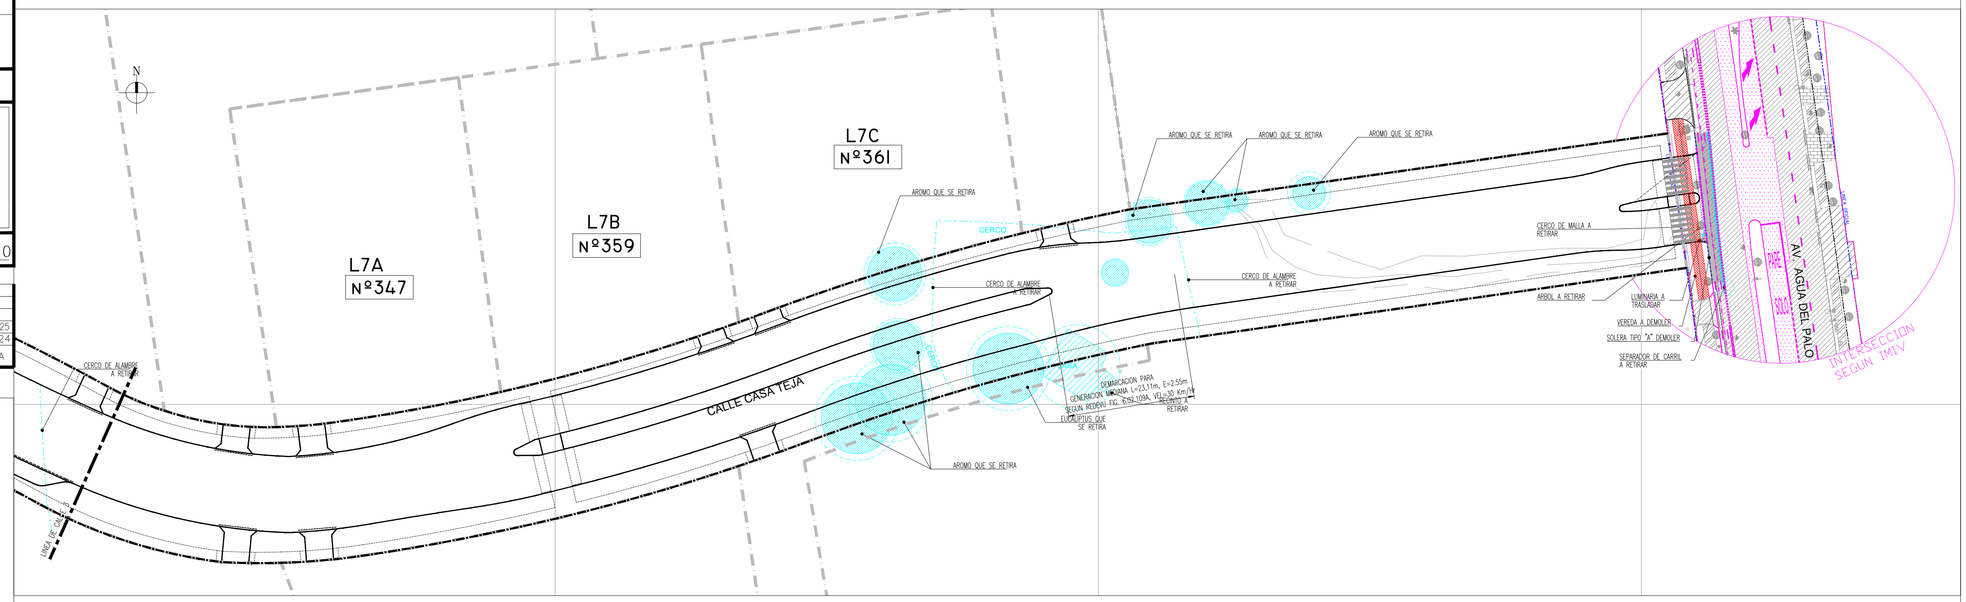

PLANTA DE UBICACION

ESCALA 1 : 5000

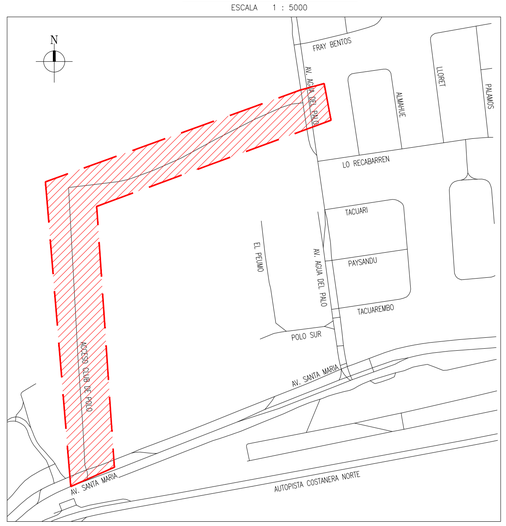

SIMBOLOGIA

- CAMARA DE INSPECCION CIRCULAR
- CAMARA DE INSPECCION RECTANGULAR
- CAMARA DE INSPECCION DOBLE
- CAMARA TELEFONICA
- CAMARA ELECTRICA RECT
- CAMARA DE AGUAS LLUVIAS
- CAMARA DE AGUAS SERVIDAS
- CAMARA DE AGUAS POTABLE
- CAMARA DE GAS
- LLAVE DE AGUA
- GRIFO
- SUMIDERO
- MEDIDOR AGUA
- LETRERO PUBLICITARIO
- POSTE DE HORMIGON
- POSTE DE MADERA
- POSTE DE FIERRO
- TENSOR
- LUMINARIA
- POSTE DE MADERA CON LUMINARIA
- POSTE DE HORM. CON LUMINARIA
- POSTE CON CAMARA DE VIGILANCIA
- PARADERO DE BUSES
- AVISO PUBLICITARIO
- ESTACION
- SEÑAL INFORMATIVA
- SEÑAL DE TRANSITO
- NOMBRE DE CALLE
- QUIOSKO

- ARBOL
- ACACIO
- CIRUELO
- LIQUIDAMBAR
- MANZANO
- ESPINO
- EUCALIPTUS
- QUILLAY
- PALMERA
- PINO

- ACCESOS
- CAMINO DE TIERRA
- CERCO DE ALAMBRE
- CERCO MALLA
- LINEA DE CIERRO
- MURO
- MURO DE VIBROCRET
- PAVIMENTO
- REJA
- SOLERA
- SOLERA REBAJADA
- SOLERA EXISTENTE
- RADIER
- PAVIMENTO EXISTENTE HCV
- LINEA OFICIAL
- VEREDAS EXISTENTES HC

OBRAS PROYECTADAS

- SOLERAS TIPO "A" PL. 0.15m
- SOLERAS TIPO "A" PL. 0.00m
- LINEA OFICIAL
- SOLERAS TIPO "C"
- BORDE DE PAVIMENTO

OBRAS DE DEMOLICION

- SOLERAS EXISTENTES A DEMOLER
- CALZADA ASFALTICA A DEMOLER
- CAMARAS A NIVELAR COTA
- VEREDAS A DEMOLER
- ELEMENTOS A TRASLADAR O RETIRAR
- CERCO DE MALLA A RETIRAR
- CERCO DE ALAMBRE A RETIRAR
- REJA A RETIRAR
- MURO A RETIRAR
- MURO DE VIBROCRET A RETIRAR

REVISION N°		EJECUTÓ	AIBUJÓ	REVISÓ	APROBÓ	FECHA
0	PARA APROBACION SERVIU	V.A.F.	V.A.F.	L.E.C.	I.M.S.	12.11.24

ARCHIVO CAD : 31802_pav ext_Urbanizacion loteo Lo Recabarren_Rev 1.dwg