SERVIU

SERVICIO DE VIVIENDA Y URBANIZACION
REGION METROPOLITANA
SUB–DIRECCION PAVIMENTACION Y OBRAS VIALES

SECCIÓN REVISIÓN E INSPECCIÓN DE PROYECTOS Y OBRAS DE PAVIMENTACIÓN Y AGUAS LLUVIAS PARTICULARES

PROYECTO DE PAVIMENTACION

URBANIZACION
LOTEO LO RECABARREN

TIPO DE VIA: SANTA MARIA (COLECTORA)
TIPO DE VIA: CAMINO AGUA DE PALO (COLECTORA)
TIPO DE VIA: CALLE CASA TEJA (LOCAL)

PLANTA DE GEOMETRIA

COMUNA	FECHA	ESCALAS
VITACURA	SEPTIEMBRE 2025	INDICADAS

PROYECTO: URBANO PROYECTOS
IVAN MUÑOZ S.–URBANO PROYECTOS
Ing. Civil U. de Ch.
Alfredo Barros Errazuriz 1953
Oficina 903 Fono 229125500

TOPOGRAFIA

LABORATORIO MECANICA DE SUELO

MANDANTE: INMOBILIARIA LO RECABARREN LTDA.

OTRO

APROBACION SERVIU METROPOLITANO

EL PRESENTE PLANO HA SIDO APROBADO POR OFICIO SERVIU
N° DE FECHA

REVISOR — INGENIERO JEFE DE SECCION

CARPETA N°74073 PLANO N° 3 DE 10

N°	MODIFICACION	FIRMA	FECHA
1	PARA APROBACION SERVIU	I.M.S.	SEP 2025
0	PARA APROBACION SERVIU	I.M.S.	12.11.24

ARCHIVO CAD : 31802_pav ext_Urbanizacion loteo Lo Recabarren_Rev 1.dwg

SIMBOLOGIA

- CAMARA DE INSPECCION CIRCULAR
- CAMARA DE INSPECCION RECTANGULAR
- CAMARA DE INSPECCION DOBLE
- CAMARA TELEFONICA
- CAMARA ELECTRICA RECT
- CAMARA DE AGUAS LLUVIAS
- CAMARA DE AGUAS SERVIDAS
- CAMARA DE AGUAS POTABLE
- CAMARA DE GAS
- LLAVE DE AGUA
- GRIFO
- SUMIDERO
- MEDIDOR AGUA
- LETRERO PUBLICITARIO
- POSTE DE HORMIGON
- POSTE DE MADERA
- POSTE DE FIERRO
- TENSOR
- LUMINARIA
- POSTE DE MADERA CON LUMINARIA
- POSTE DE HORM. CON LUMINARIA
- POSTE CON CAMARA DE VIGILANCIA
- PARADERO DE BUSES
- AVISO PUBLICITARIO
- ESTACION
- SEÑAL INFORMATIVA
- SEÑAL DE TRANSITO
- NOMBRE DE CALLE
- QUIOSKO

- ARBOL
- ACACIO
- CIRUELO
- LIQUIDAMBAR
- MANZANO
- ESPINO
- EUCALIPTUS
- QUILLAY
- PALMERA
- PINO

- ACCESOS
- CAMINO DE TIERRA
- CERCO DE ALAMBRE
- CERCO MALLA
- LINEA DE CIERRO
- MURO
- MURO DE VIBROCRET
- PAVIMENTO
- REJA
- SOLERA EXISTENTE
- RADIER
- PAVIMENTO EXISTENTE HCV
- LINEA OFICIAL
- VEREDAS EXISTENTES HC


OBRAS PROYECTADAS

- SOLERAS TIPO "A" PL. 0.15m
- SOLERAS TIPO "A" PL. 0.00m
- SOLERAS TIPO "C"
- BORDE DE PAVIMENTO
- SUMIDERO TIPO S2
- SUMIDERO TIPO BATERIA
- VEREDA HC
- CALZADA HCV
- BALDOSA MINVU 0
- SEPARACION PROYECTADA CICLOVIA
- DEMARCACION PROYECTADA CICLOVIA
- CAMARA PROYECTADA


PROYECTO SERVIU CODIGO N°63023

- CALZADA HCV
- VEREDA HC
- SOLERA TIPO "A"

PLANTA DE GEOMETRIA
ESCALA 1 : 500

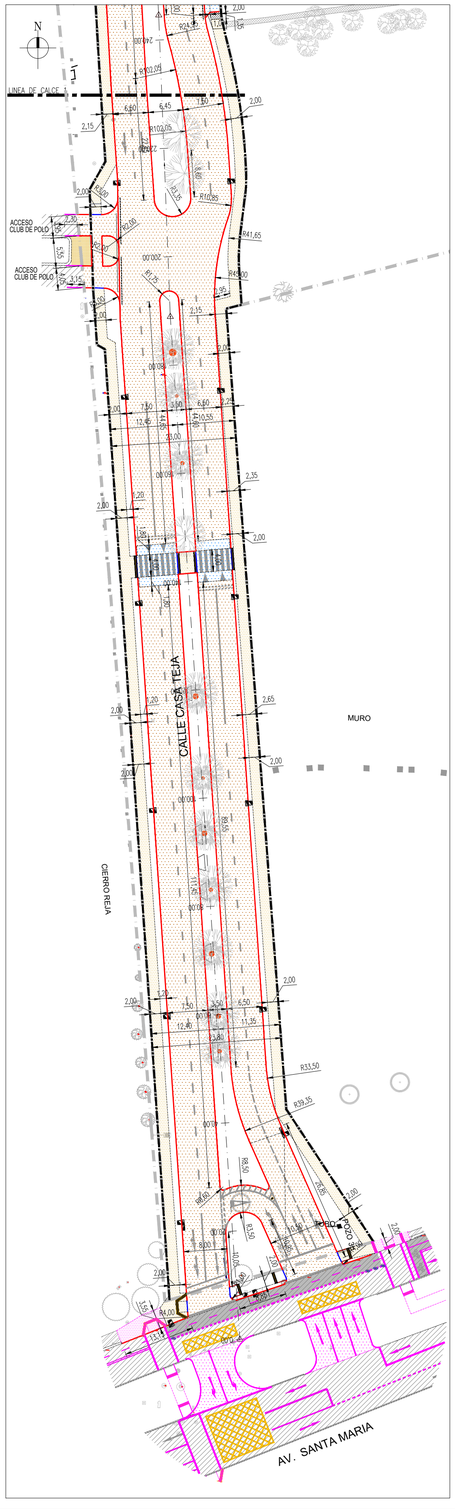


PLANTA DE GEOMETRIA
ESCALA 1 : 500

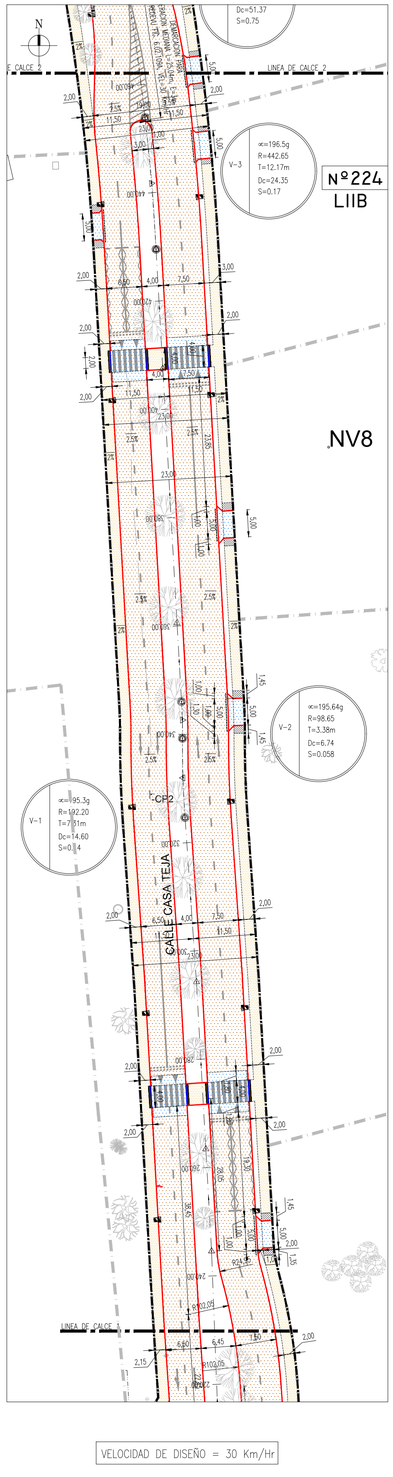

VELOCIDAD DE DISEÑO = 30 Km/Hr

PLANTA DE GEOMETRIA
ESCALA 1 : 500

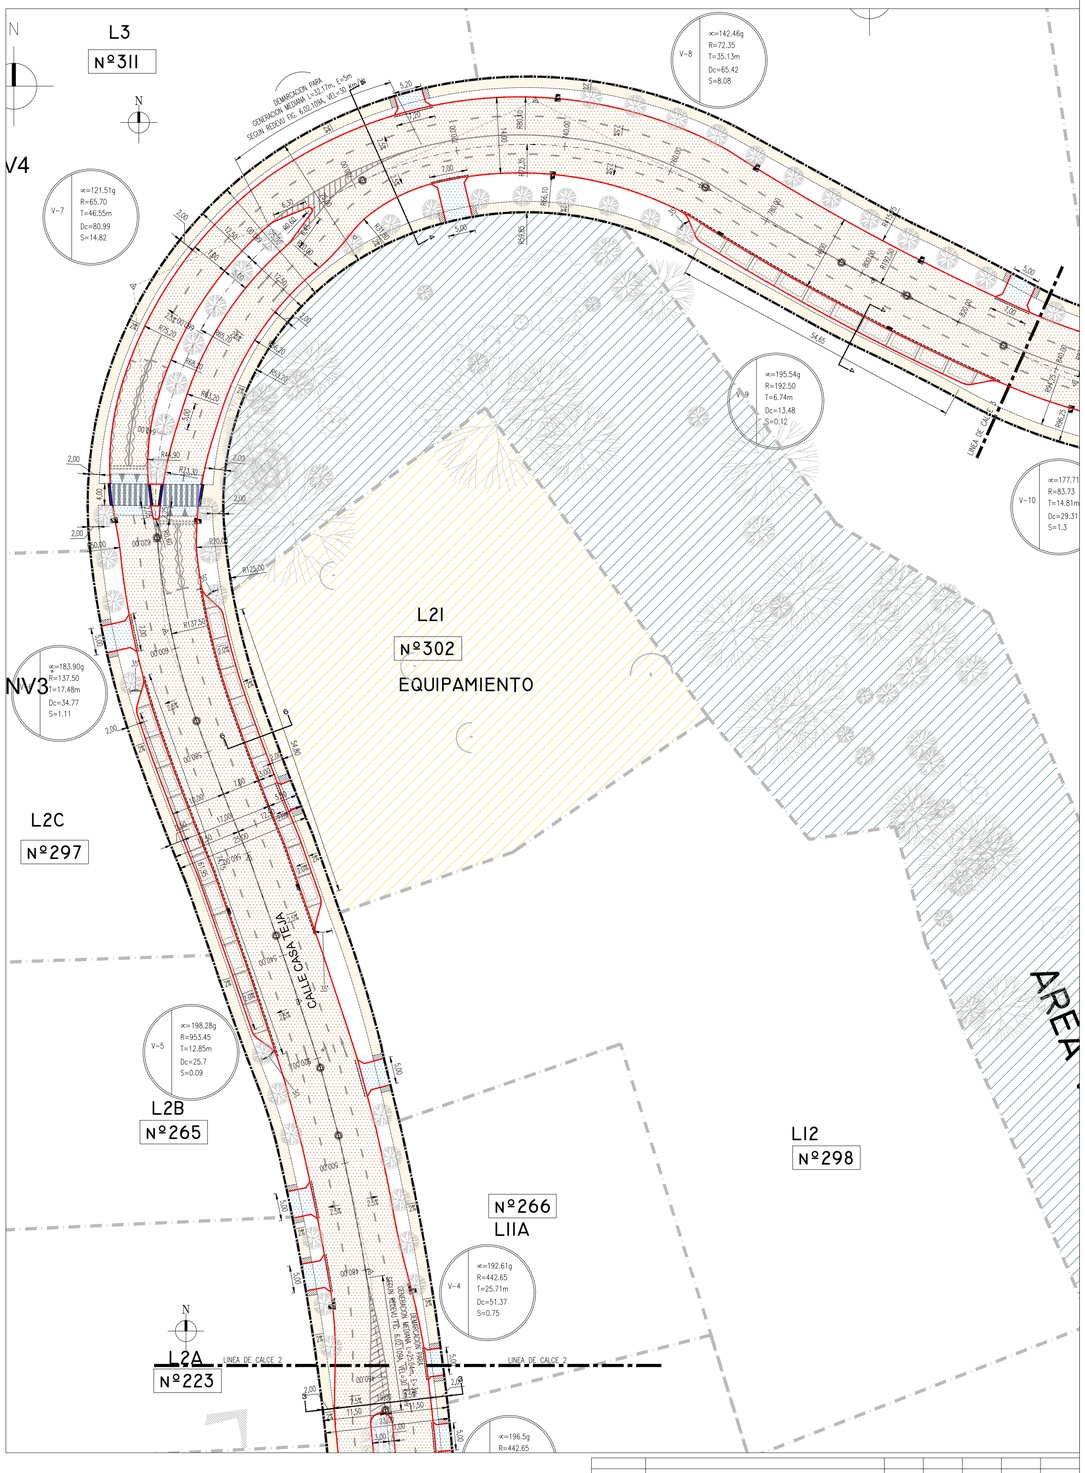

REVISION N°		EJECUTÓ	AIBUJÓ	REVISÓ	APROBÓ	FECHA
0	PARA APROBACION SERVIU	V.A.F.	V.A.F.	L.E.C.	I.M.S.	12.11.24

ARCHIVO CAD : 31802_pav ext_Urbanizacion loteo Lo Recabarren_Rev 1.dwg