SERVIU

SERVICIO DE VIVIENDA Y URBANIZACION
REGION METROPOLITANA
SUB–DIRECCION PAVIMENTACION Y OBRAS VIALES

SECCIÓN REVISIÓN E INSPECCIÓN DE PROYECTOS Y OBRAS DE PAVIMENTACIÓN Y AGUAS LLUVIAS PARTICULARES

PROYECTO DE PAVIMENTACION

URBANIZACION
LOTEO LO RECABARREN

TIPO DE VIA: SANTA MARIA (COLECTORA)
TIPO DE VIA: CAMINO AGUA DE PALO (COLECTORA)
TIPO DE VIA: CALLE CASA TEJA (LOCAL)

PERFIL LONGITUDINAL CALLE

COMUNA	FECHA	ESCALAS
VITACURA	SEPTIEMBRE 2025	INDICADAS

PROYECTO		TOPOGRAFIA
URBANO PROYECTOS	IVAN MUÑOZ S.–URBANO PROYECTOS Ing. Civil U. de Ch. Alfredo Barros Errazuriz 1953 Oficina 903 Fono 229125500	
LABORATORIO MECANICA DE SUELO	MANDANTE	OTRO
	INMOBILIARIA LO RECABARREN LTDA.	

APROBACION SERVIU METROPOLITANO

EL PRESENTE PLANO HA SIDO APROBADO POR OFICIO SERVIU
N° DE FECHA

REVISOR — INGENIERO JEFE DE SECCION


CARPETA N°74073 PLANO N° 5 DE 10

N°	MOAIFICACION	FIRMA	FECHA
1	PARA APROBACION SERVIU	I.M.S.	SEP 2025
0	PARA APROBACION SERVIU	I.M.S.	12.11.24

PERFIL LONGITUDINAL (Km 0+000 - 0+300.00)

ESCALA H=1:500
V=1:200

VELOCIDAD DE DISEÑO = 30 Km/Hr

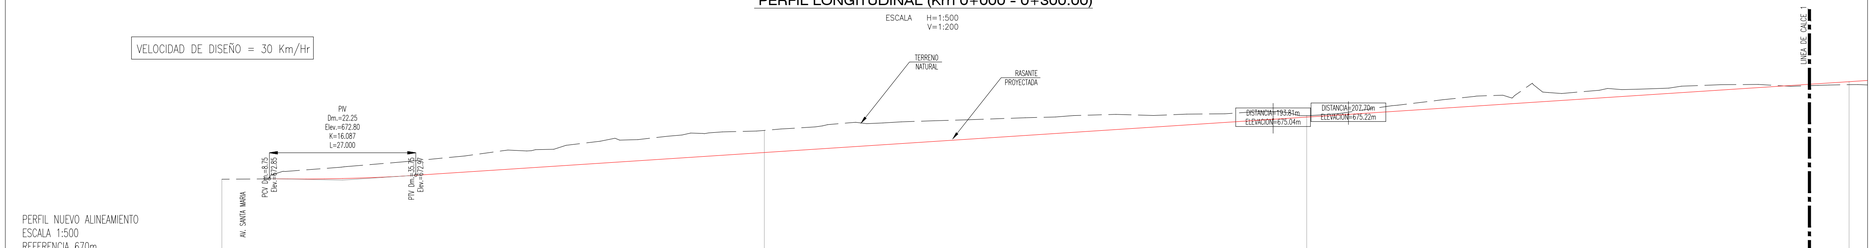


PERFIL NUEVO ALINEAMIENTO
ESCALA 1:500
REFERENCIA 670m

DISTANCIA PARCIAL [m]	8.75	13.50	13.50	64.25	100.00	100.00		
DISTANCIA ACUMULADA [m]	0.00	8.75	22.25	35.75	100.00	200.00	300.00	
ELEVACION TERRENO[m]	672.85	673.28	673.51	674.83	675.17	676.31		
ELEVACION RASANTE [m]	INFINITY	672.85	672.97	673.81	675.12	676.42		
PENDIENTE (i) / LONGITUD (L)	i=0.00% L=0.00	2T=27.00m K=1608.67m L=27.00m		i=1.31% L=299.87				

PERFIL LONGITUDINAL (Km 0+300 - 0+660.96)

ESCALA H=1:500
V=1:200

VELOCIDAD DE DISEÑO = 30 Km/Hr

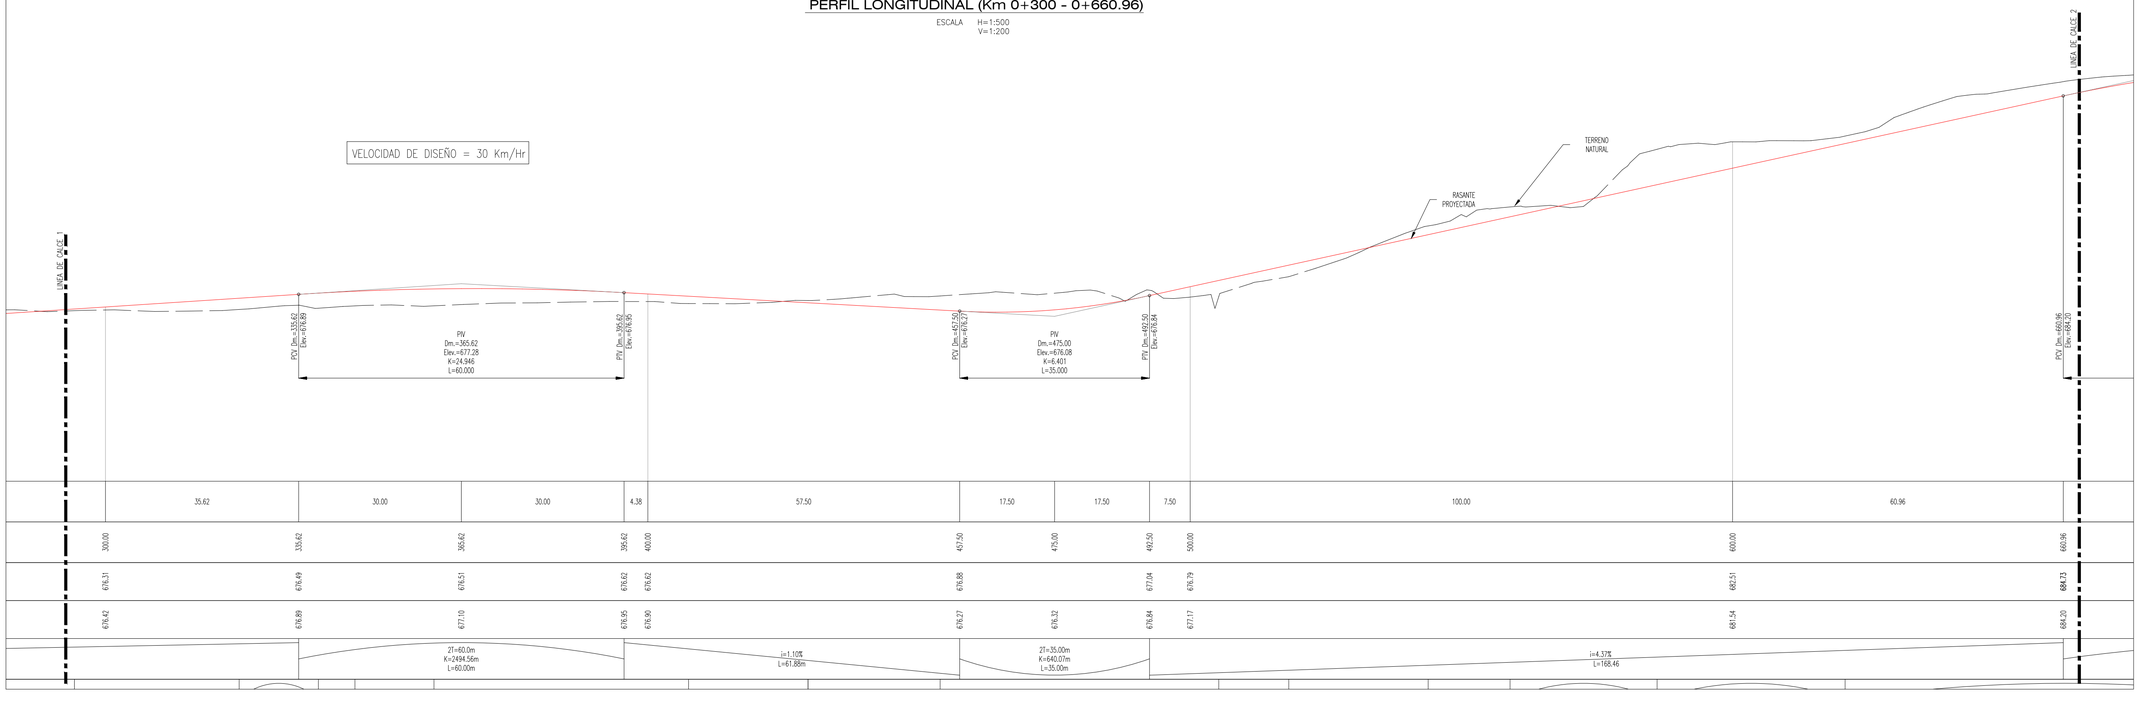

	35.62	30.00	30.00	4.38	57.50	17.50	17.50	7.50	100.00	60.96				
300.00	335.62	365.62	395.62	400.00	457.50	475.00	492.50	500.00	600.00	660.96				
676.31	676.49	676.51	676.62	676.62	676.88	677.04	676.79	682.51	684.73					
676.42	676.89	677.10	676.95	676.90	676.27	676.32	676.84	677.17	681.54	684.20				
		2T=60.0m K=2494.56m L=60.00m		i=1.10% L=61.88m		2T=35.00m K=640.07m L=35.00m		i=4.37% L=168.46						

REVISION N°		EJECUTÓ	AIBUJÓ	REVISÓ	APROBÓ	FECHA
0	PARA APROBACION SERVIU	V.A.F.	V.A.F.	L.E.C.	I.M.S.	12.11.24

ARCHIVO CAD : 31802_pav ext_Urbanizacion lotea Lo Recabarren_Rev 1.dwg