SERVIU

SERVICIO DE VIVIENDA Y URBANIZACION
REGION METROPOLITANA
SUB-DIRECCION PAVIMENTACION Y OBRAS VIALES

SECCIÓN REVISIÓN E INSPECCIÓN DE PROYECTOS Y OBRAS DE PAVIMENTACIÓN Y AGUAS LLUVIAS PARTICULARES

PROYECTO DE PAVIMENTACION

URBANIZACION
LOTEO LO RECABARREN

TIPO DE VIA: SANTA MARIA (COLECTORA)
TIPO DE VIA: CAMINO AGUA DE PALO (COLECTORA)
TIPO DE VIA: CALLE CASA TEJA (LOCAL)

PERFIL LONGITUDINAL (CONTINUACION)

COMUNA	FECHA	ESCALAS
VITACURA	SEPTIEMBRE 2025	INDICADAS

PROYECTO: URBANO PROYECTOS
IVAN MUÑOZ S.-URBANO PROYECTOS
Ing. Civil U. de Ch.
Alfredo Barros Errazuriz 1953
Oficina 903 Fono 229125500

TOPOGRAFIA

LABORATORIO MECANICA DE SUELO

MANDANTE: INMOBILIARIA LO RECABARREN LTDA.

OTRO

APROBACION SERVIU METROPOLITANO

EL PRESENTE PLANO HA SIDO APROBADO POR OFICIO SERVIU
N° DE FECHA

REVISOR | INGENIERO JEFE DE SECCION


CARPETA N°74073 PLANO N° 6 DE 10

N°	MODIFICACION	FIRMA	FECHA
1	PARA APROBACION SERVIU	I.M.S.	SEP 2025
0	PARA APROBACION SERVIU	I.M.S.	12.11.24

ARCHIVO CAD : 31802_pav ext_Urbanizacion loteo Lo Recabarren_Rev 1.dwg


PERFIL LONGITUDINAL (Km 0+660.96 - 1+000)

ESCALA H=1:500 V=1:200

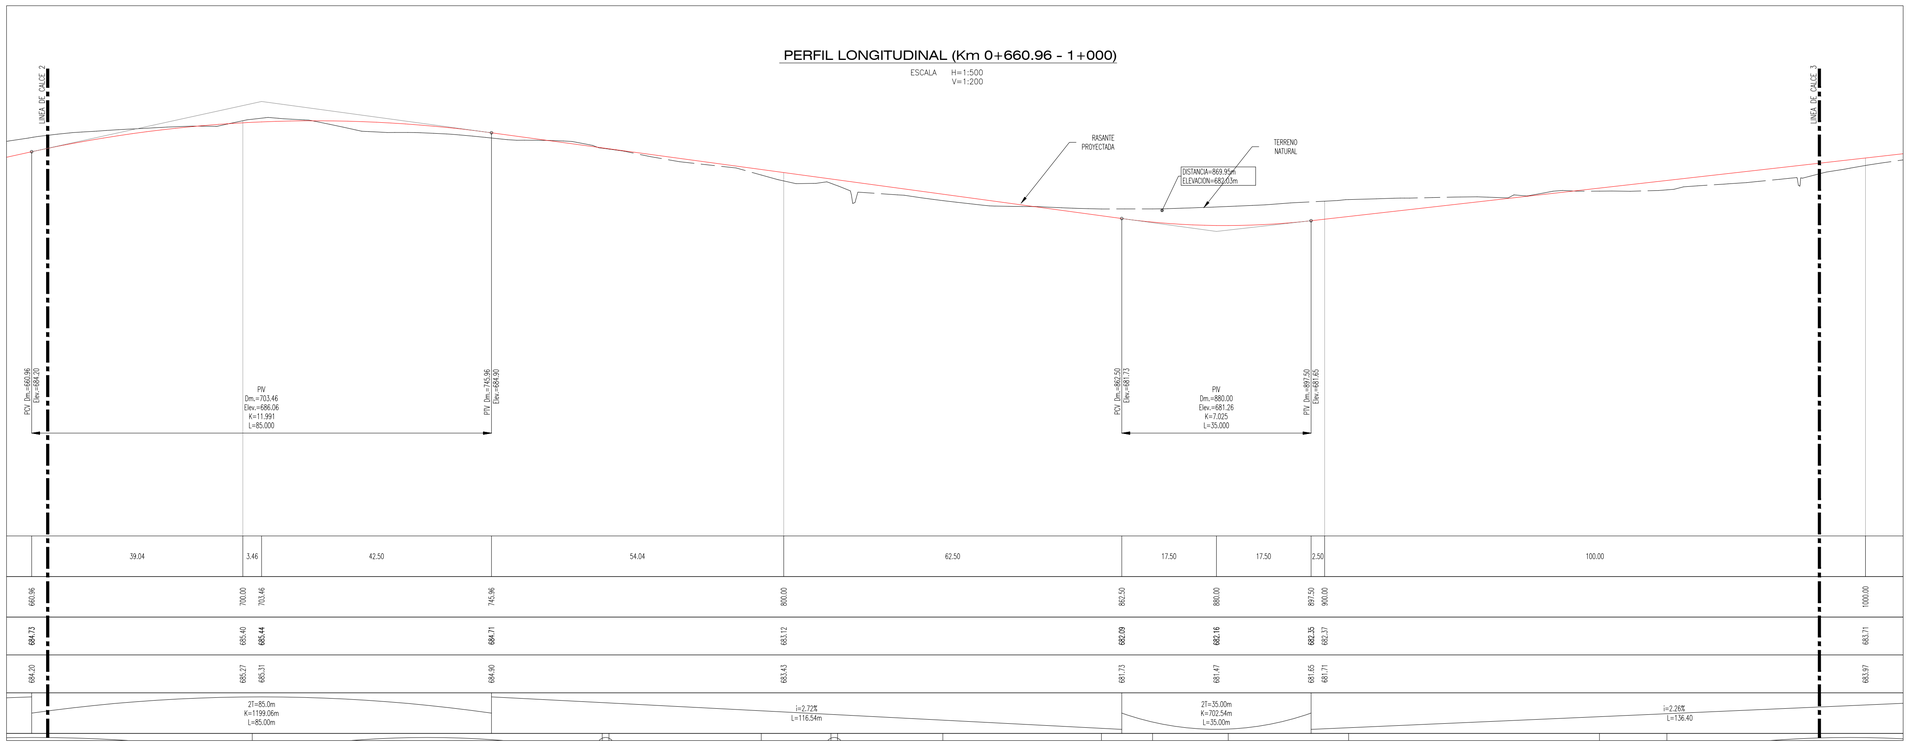

PERFIL LONGITUDINAL (Km 1+000 - 1+140.58)

ESCALA H=1:500 V=1:200

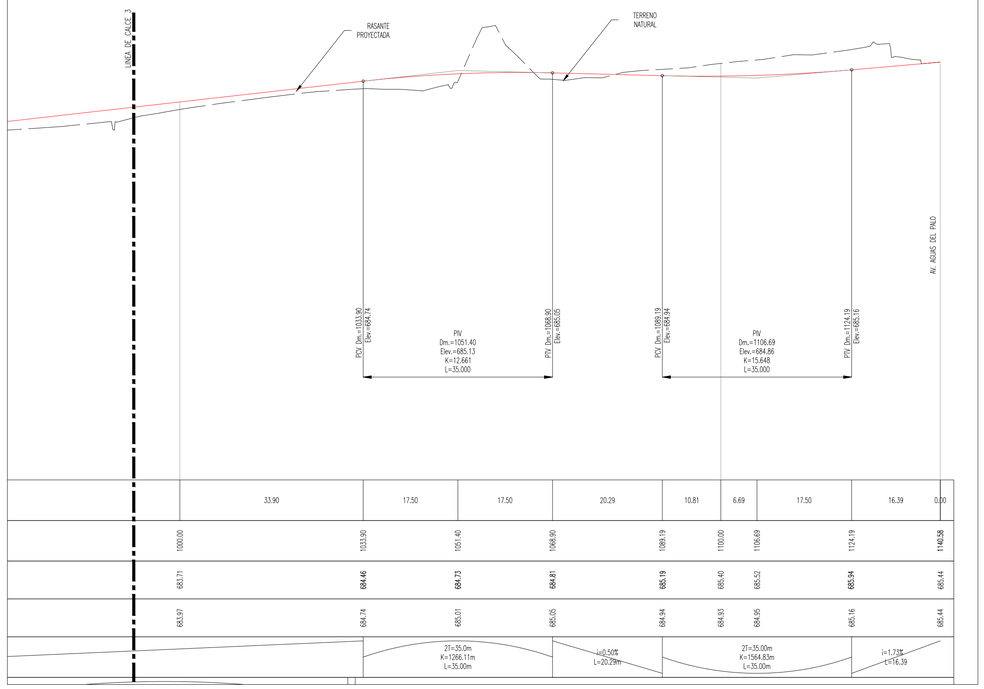

VELOCIDAD DE DISEÑO = 30 Km/Hr

REVISION N°	MODIFICACION	EJECUTÓ	AIBUJÓ	REVISÓ	APROBÓ	FECHA
0	PARA APROBACION SERVIU	V.A.F.	V.A.F.	L.E.C.	I.M.S.	12.11.24

ARCHIVO CAD : 31802_pav ext_Urbanizacion loteo Lo Recabarren_Rev 1.dwg